

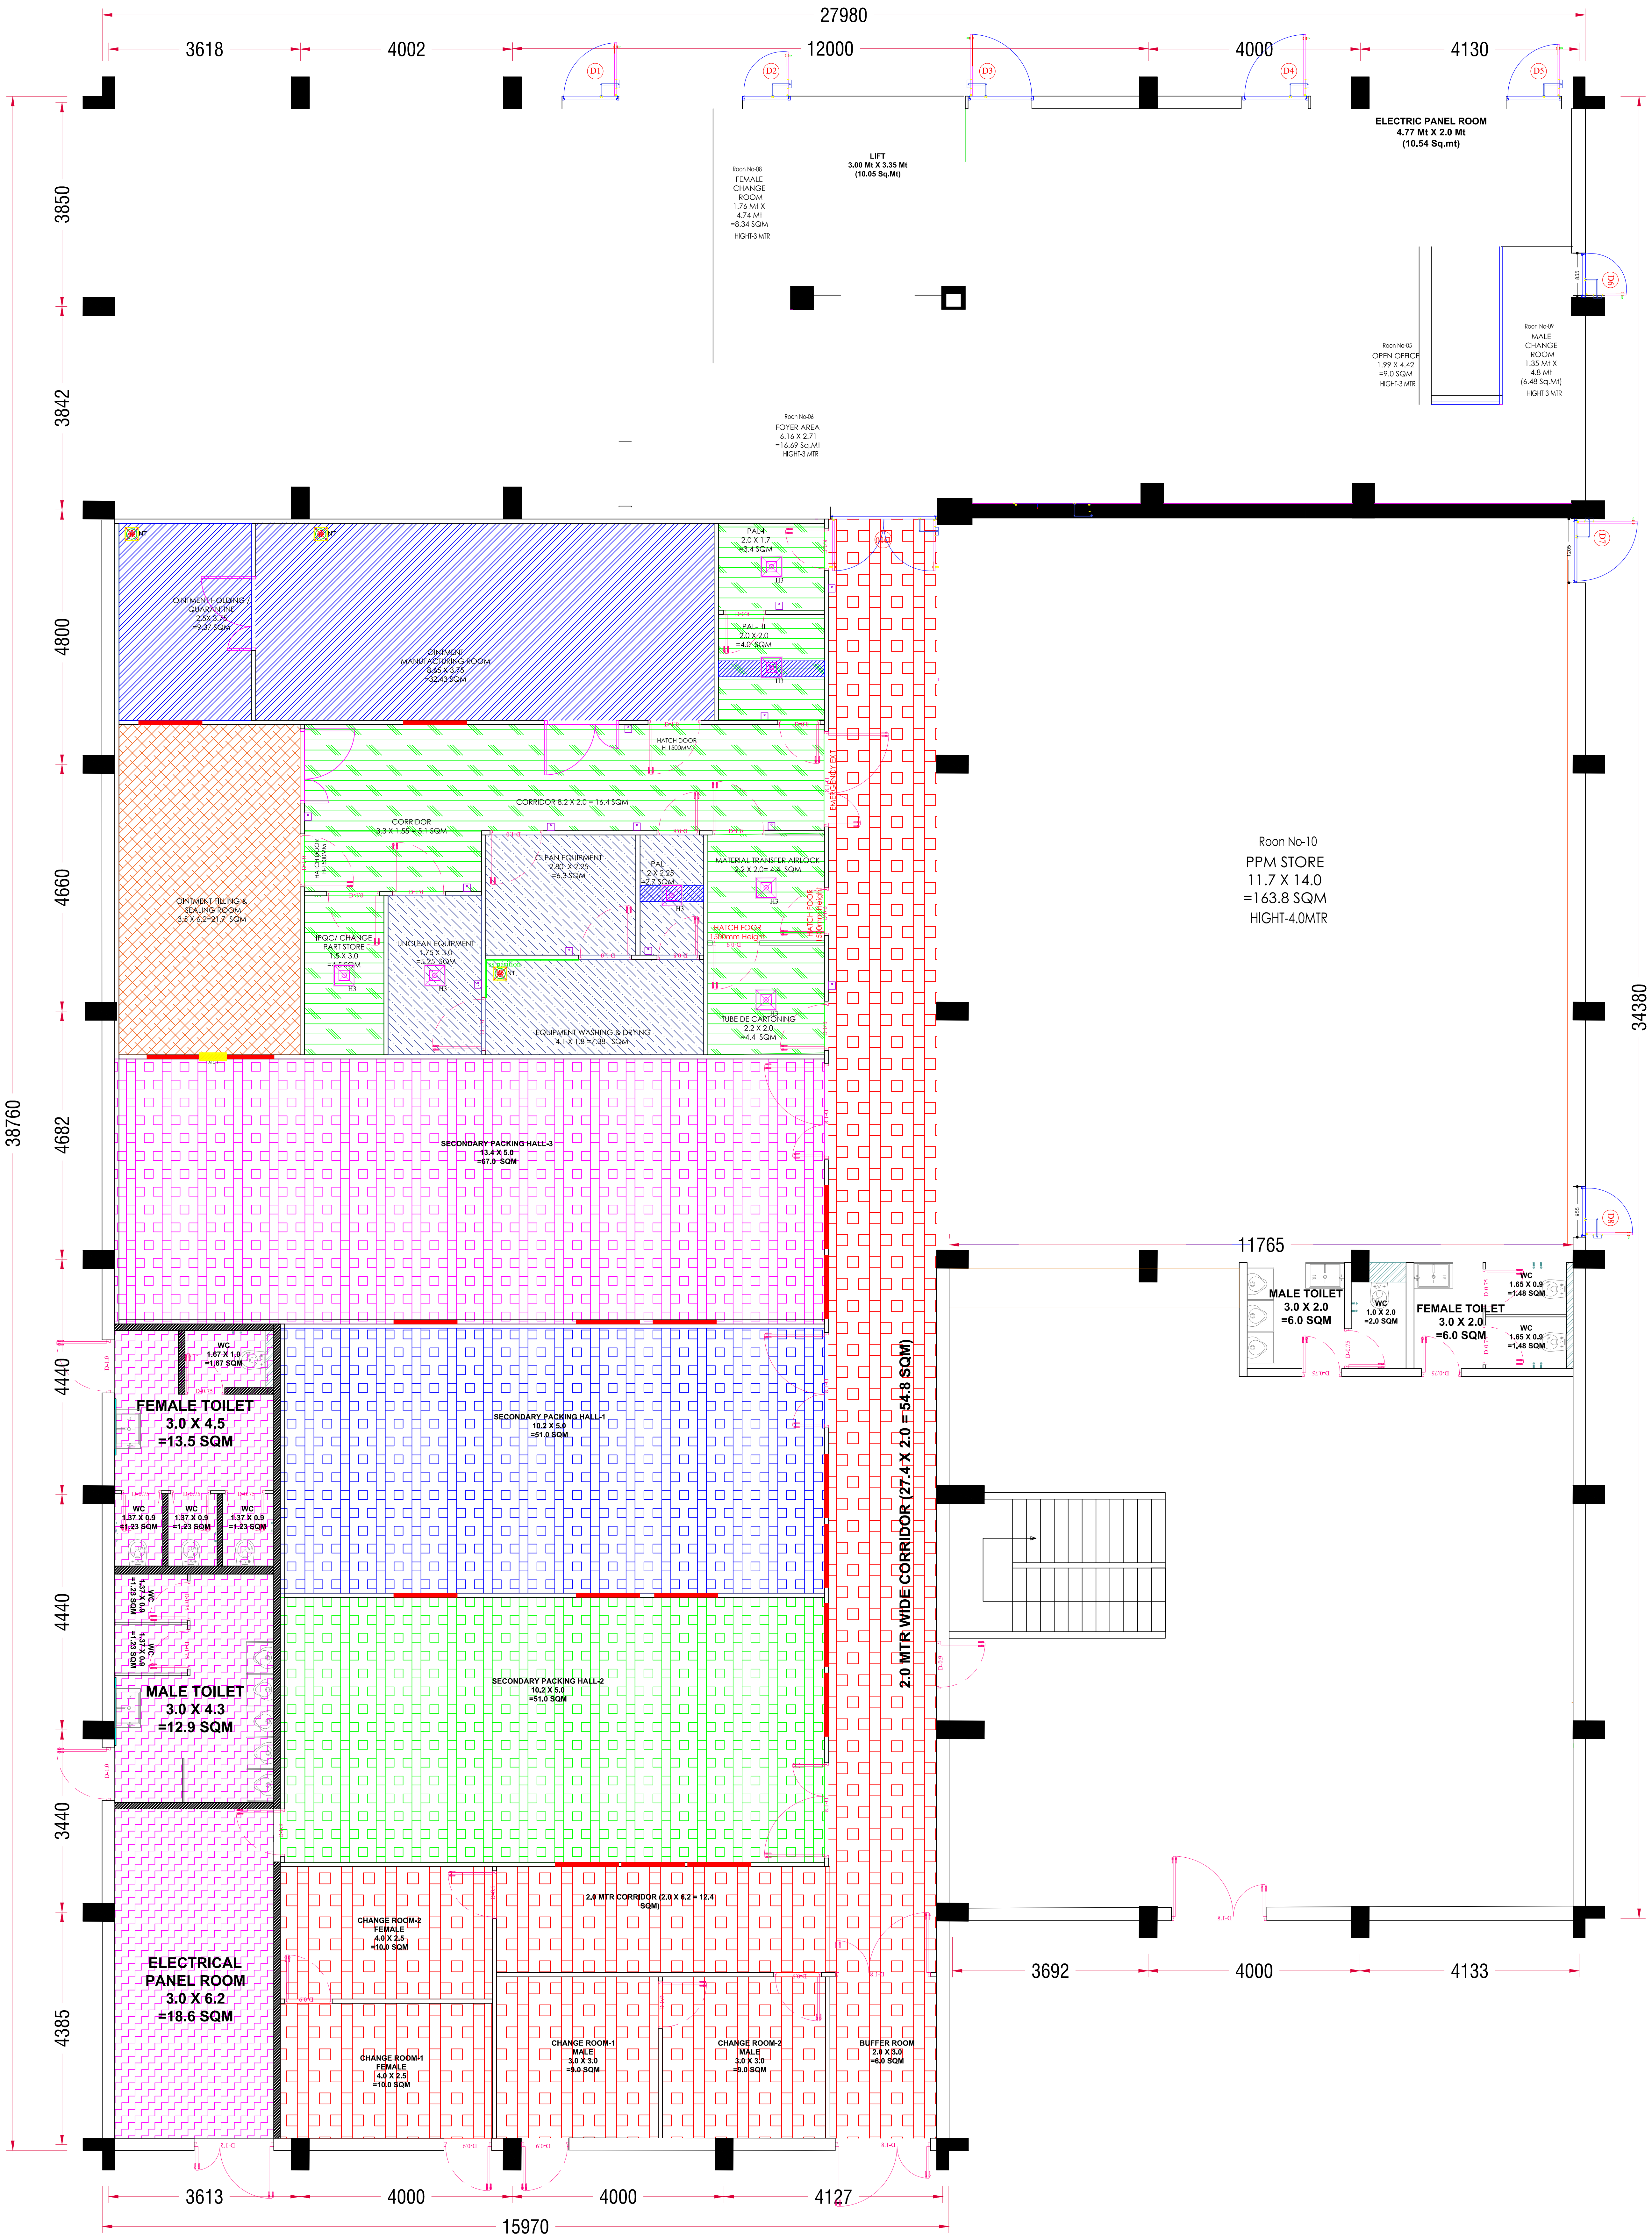


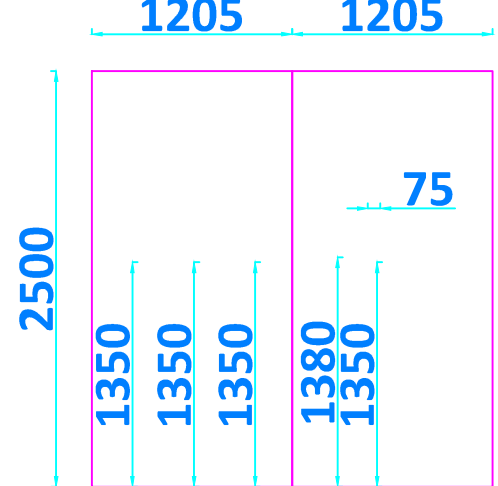

Room No-10
PPM STORE
11.7 X 14.0
=163.8 SQM
HIGHT-4.0MTR

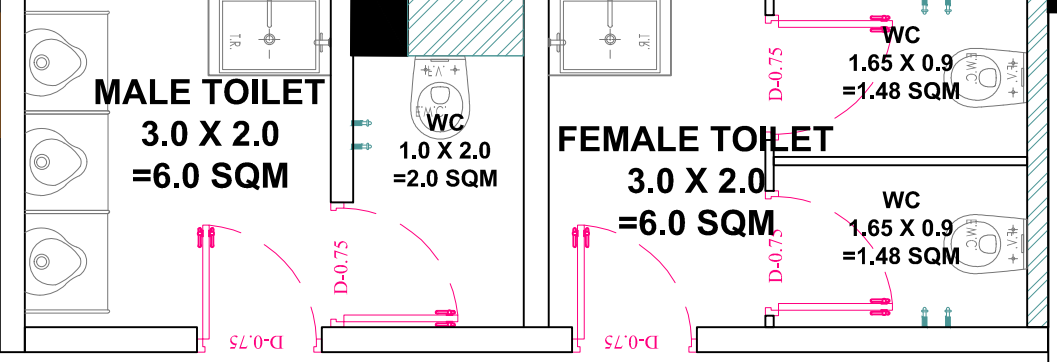

AREA CLASSIFICATION			
CLASSIFICATION	CLASS-A	CLASS-B	CLASS-C
CLASS 100	UNDER LAF	PRE FILTER 10 µ + FINE FILTER 5 µ + PLENUM FILTER 0.3 µ	HEPA 0.3 µ
CLASS 1,000	PRE FILTER 10 µ + FINE FILTER 5 µ	HEPA 0.3 µ	HEPA 0.3 µ
CLASS 10,000	PRE FILTER 10 µ + FINE FILTER 5 µ	HEPA 0.3 µ	HEPA 0.3 µ
CLASS 100,000	PRE FILTER 10 µ + FINE FILTER 5 µ	HEPA 0.3 µ	HEPA 0.3 µ
5 MICRON FILTERED AIR	CNC	PRE FILTER 10 µ + FINE FILTER 5 µ + AC	CNC
SPLIT AIR CONDITIONER	SP-AC	NA	NA
EXHAUST FAN	EXT	NA	NA

AHU ZONING LEGEND

SR NO.	SYSTEM NAME	SYMBOL	TEMP.	RH NMT	REMARK
1	AHU - 01		NMT25°C	60%	CLASS-D
2	AHU - 02		NMT25°C	60%	CLASS-D
3	AHU - 03		NMT25°C	NA	CLASS-D
4	AHU - 04		NMT25°C	NA	CLASS-D
5	AHU - 05		NMT27°C	NA	CNC -5 MICRON
6	AHU - 5A		NMT27°C	NA	CNC -5 MICRON
7	AHU - 5B		NMT27°C	NA	CNC -5 MICRON
8	AHU - 5C		NMT27°C	NA	CNC -5 MICRON
A	AC		25±2°C	50±5%	CASSETTE AC
B	EXHAUST		NA	NA	EXT FAN

REV	DATE	REVISION	DRN	CHD
136				
PROJECT NO. SMB GMP136-R12				
SCALE 1:1				
APPROVED MMD				
CHECKED ANS				
DRAWN NIB				
INITIALS SIGNATURE DATE				
TITLE ROOM HEIGHT LAYOUT				
PROJECT GROUND FLOOR PLAN				
CLIENT INDIANA OPTALMIC				
CLIENT 301, Matrix Tower, Pratiksha Nagar, Ahmedabad, Gujarat-380051				
SMB CONSULTANTS & ENGINEERS				
301, Matrix Tower, Pratiksha Nagar, Ahmedabad, Gujarat-380051				
WAB - www.smbconsultants.in				
Email - info@smbconsultants.in				
THESE DRAWINGS ARE THE PROPERTY OF SMB CONSULTANTS & ENGINEERS. NO PART THEREOF SHALL BE REPRODUCED OR TRANSMITTED IN ANY FORM OR BY ANY MEANS, ELECTRONIC OR MECHANICAL, WITHOUT THE WRITTEN PERMISSION OF SMB CONSULTANTS & ENGINEERS.				